
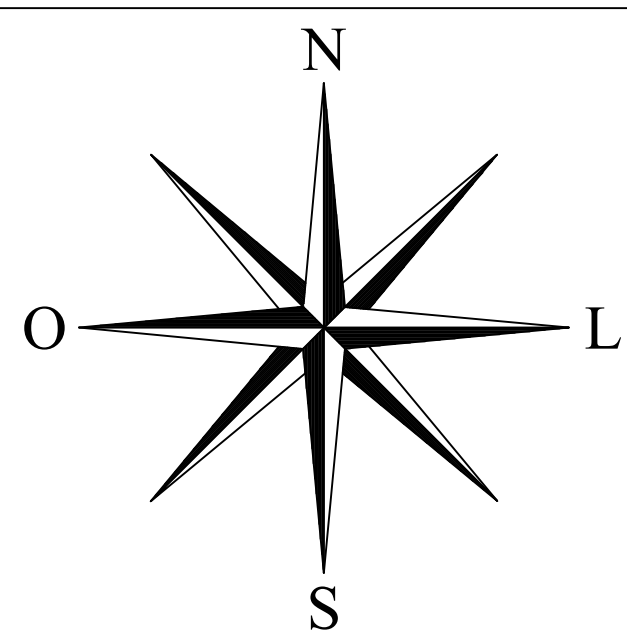
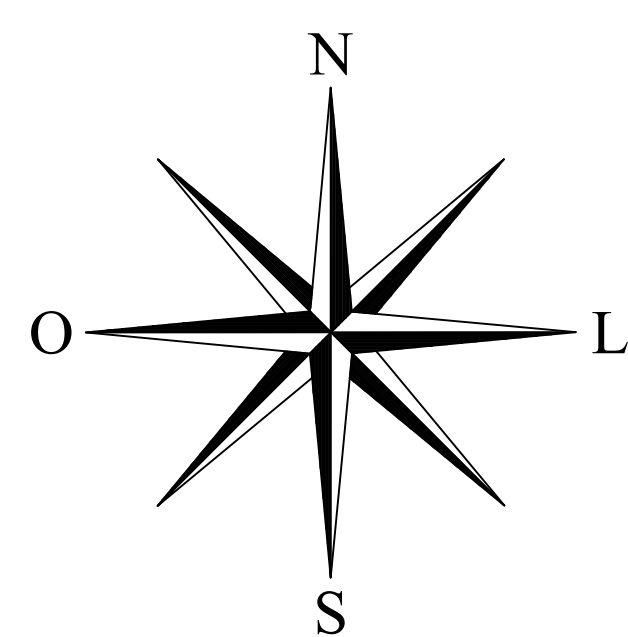


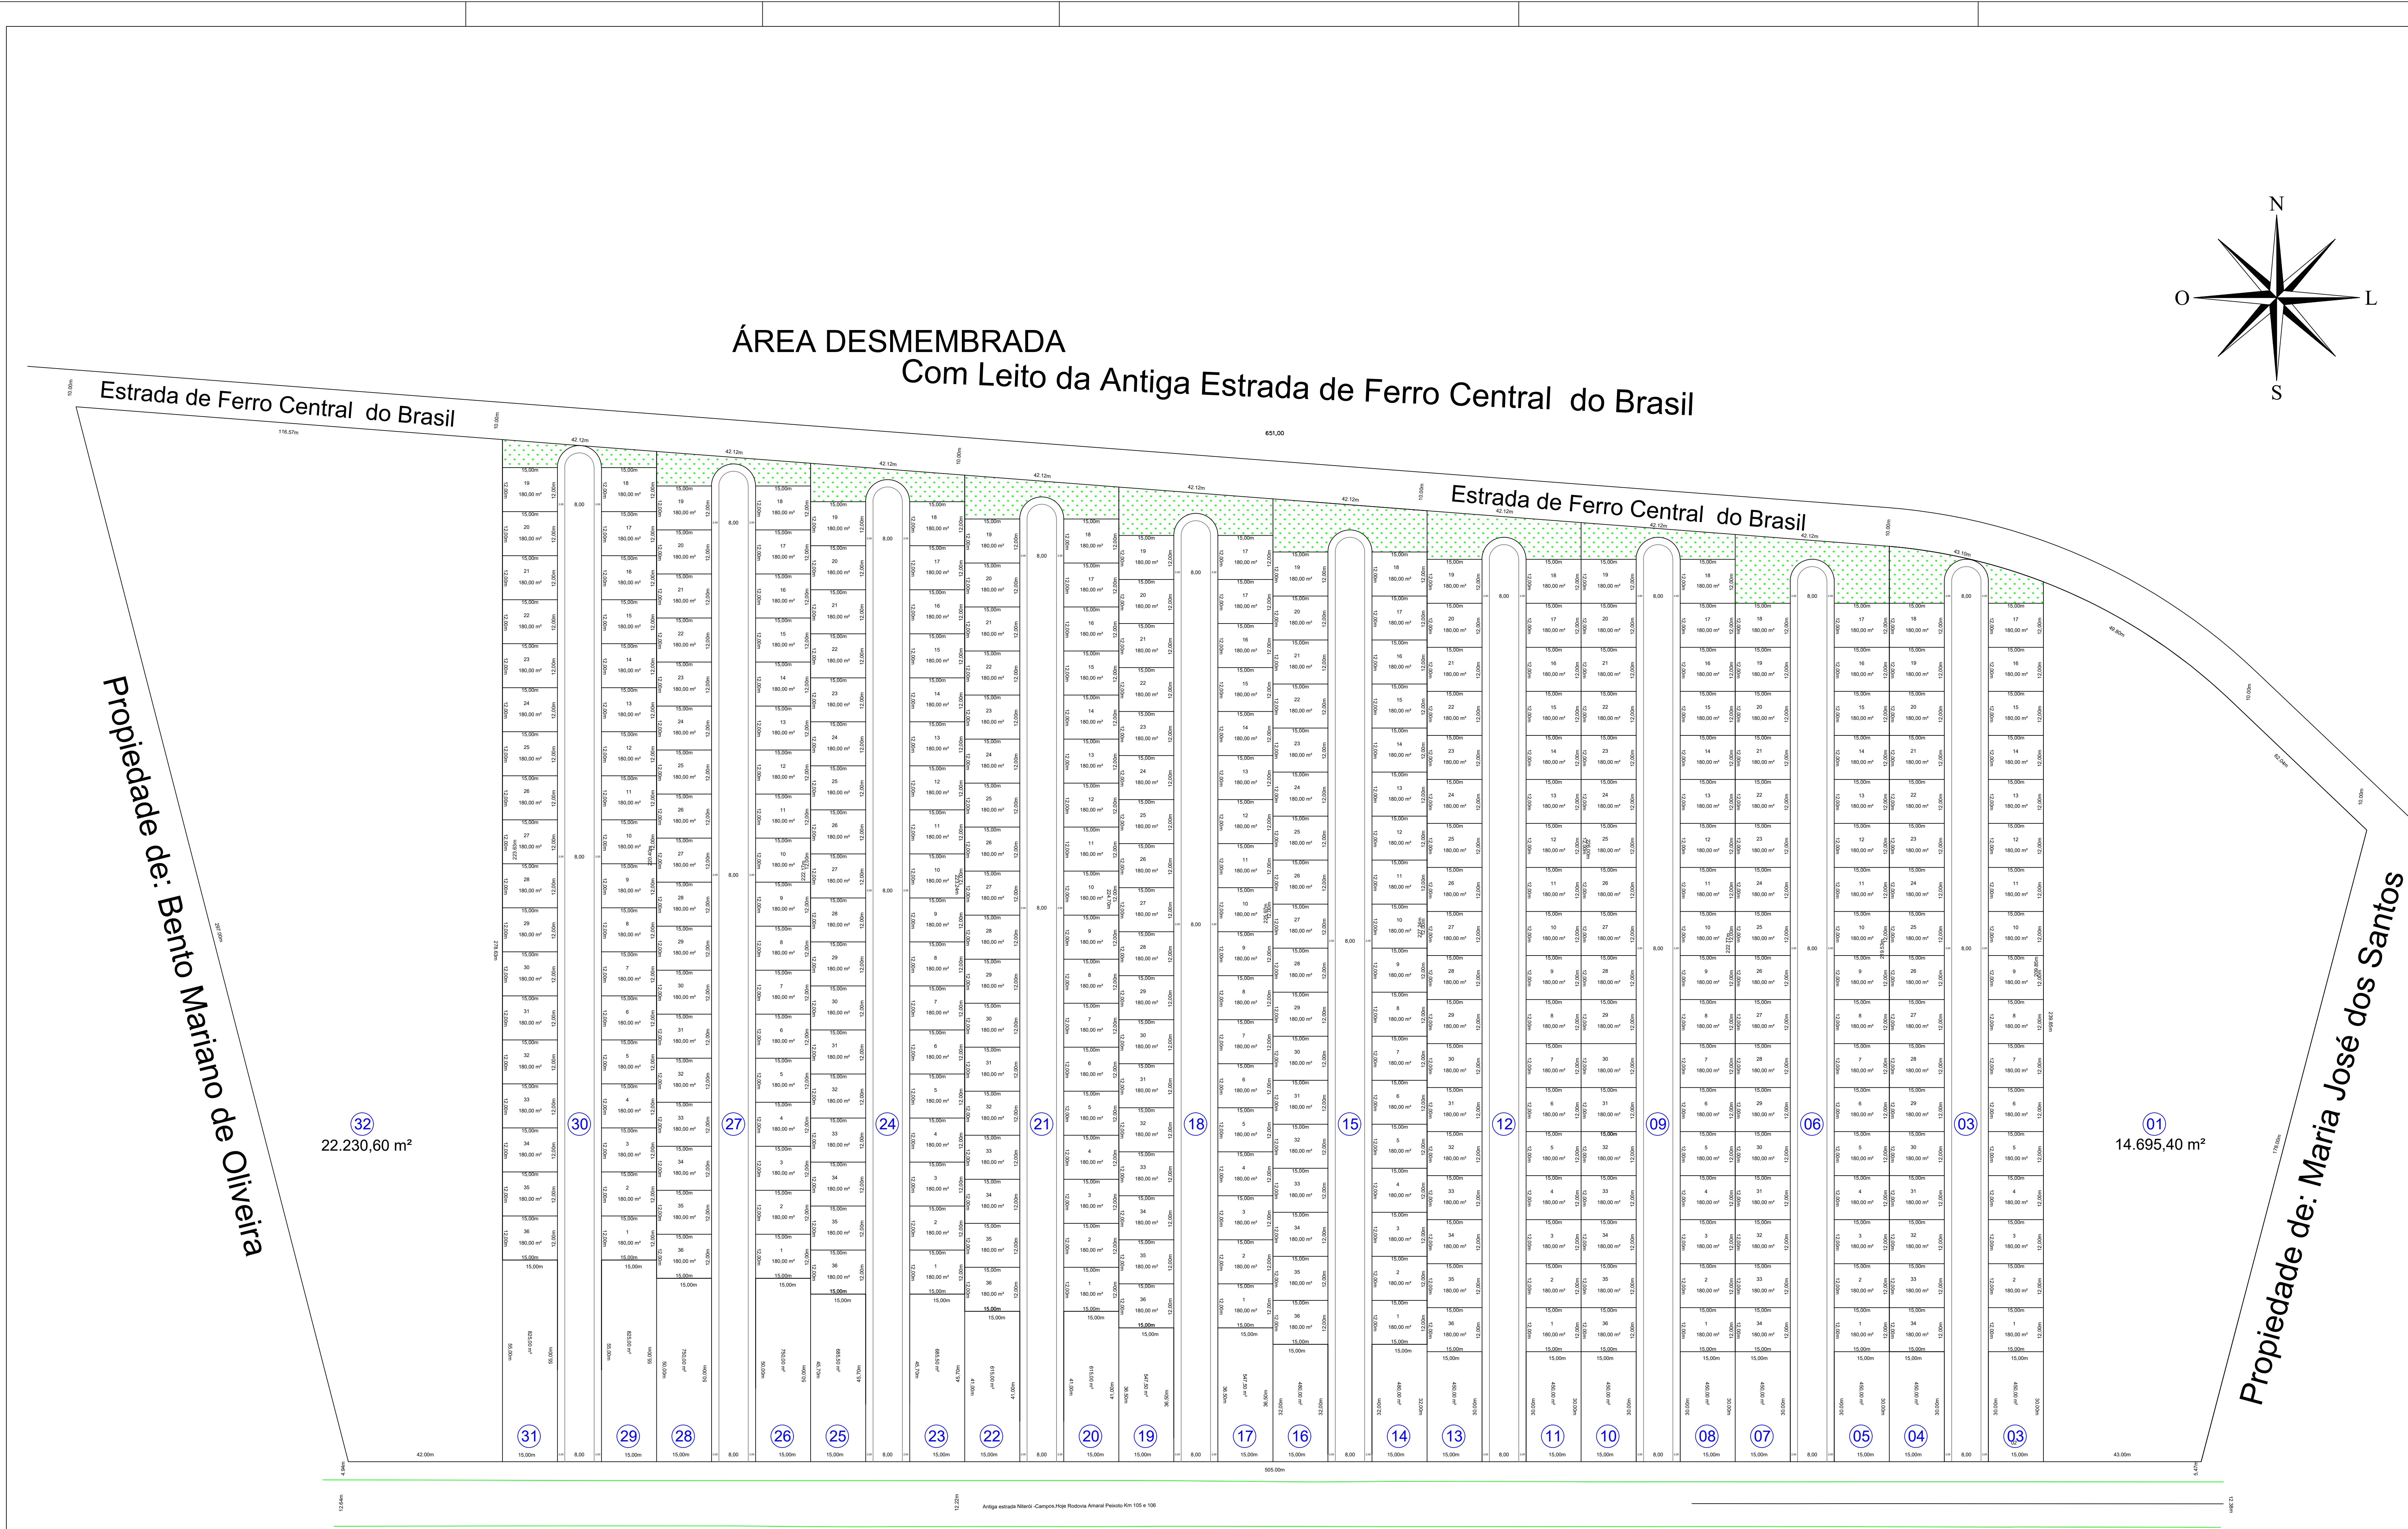

QUADRO DE ÁREAS
A DESMEMBRAR:

ÁREA----- 147.071,31m²

DESCRIÇÃO	METRAGEM QUADRADA
DESMEMBRADO	
ÁREA 01	14.695,40 m²
ÁREA 02	450,00 m²
ÁREA 03	9.420,71m²
ÁREA 04	450,00 m²
ÁREA 05	450,00 m²
ÁREA 06	9.648,32m²
ÁREA 07	450,00 m²
ÁREA 08	450,00 m²
ÁREA 09	9.784,26 m²
ÁREA 10	450,00 m²
ÁREA 11	450,00 m²
ÁREA 12	9.920,05 m²
ÁREA 13	450,00 m²
ÁREA 14	480,00 m²
ÁREA 15	9.995,84 m²
ÁREA 16	480,00 m²
ÁREA 17	547,50 m²
ÁREA 18	9.996,63 m²
ÁREA 19	547,50 m²
ÁREA 20	615,00 m²
ÁREA 21	9.997,40 m²
ÁREA 22	615,00 m²
ÁREA 23	685,50 m²
ÁREA 24	9.992,19 m²
ÁREA 25	685,50 m²
ÁREA 26	750,00 m²
ÁREA 27	9.998,97 m²
ÁREA 28	750,00 m²
ÁREA 29	825,00 m²
ÁREA 30	9.984,94 m²
ÁREA 31	825,00 m²
ÁREA 32	22.230,60 m²
ÁREA TOTAL	147.071,31m²

PROJETO DE DESMEMBRAMENTO

Projeto para desmembramento de uma área de terras situada em Sapeatiba, Zona Urbana do 1º distrito deste município de São Pedro da Aldeia-RJ

PROPRIETÁRIO Leal Porto Empreendimentos Imobiliários LTDA

QUADRO DE ÁREAS:

Leal porto empreendimento imobiliário
Lda CNPJ 03.157.471/0001-04
Representante
Walmir Leal Porto
CPF:856.180.807-10

VER QUADRO ACIMA

Autor do projeto e Responsável Técnico
KLEBER NOGUEIRA VIEIRA
CREA-RJ: 1988102262

DECLARO QUE A APROVAÇÃO DO PROJETO PELA PRESTEFURA NÃO IMPLICA NO RECONHECIMENTO DO DIREITO DE PROPRIEDADE DO TERRENO.

P.M.S.P.A.